POZIOM -1

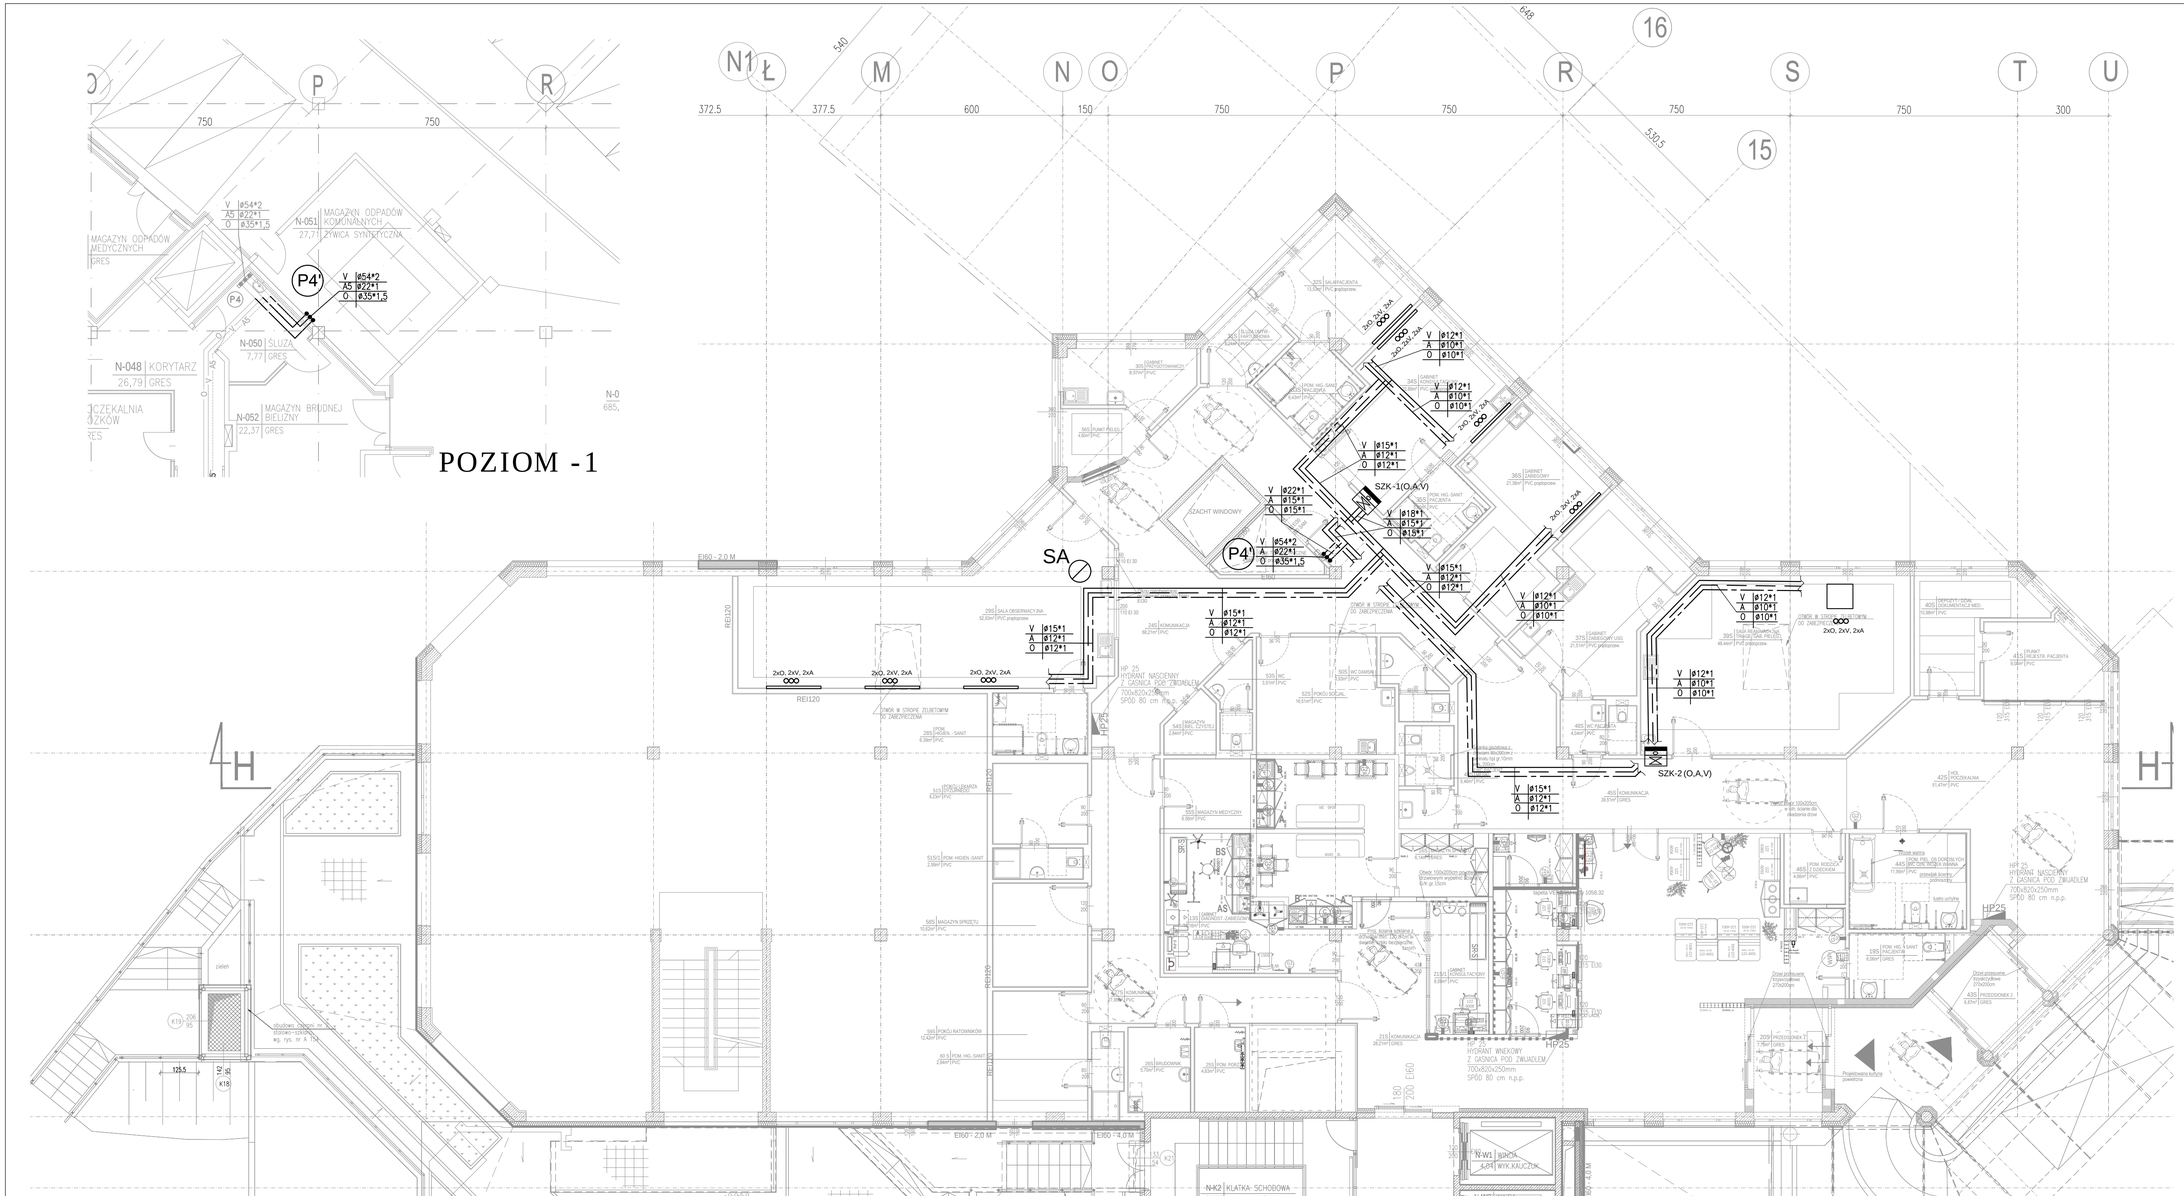

Sygnalizator zewnętrzny typ SA prod. GAZMED

Strefowe zespoły kontrolne typ SZK prod. GAZMED

przewody istniejące

przewody projektowane

pion istniejący

pion projektowany

NUMER RYSUNKU	SSE-PW-GM-01

Tresc rysunku

RZUT PARTERU
INSTALACJA GAZÓW MEDYCZNYCH

Zamierzenie

ZMIANA UKŁADU POMIESZCZEŃ I ARANŻACJI CZĘŚCI PARTERU BUDYBKU SZPITALA LUX MED

przy ul. Goszczyńskiego 1
02-616 Warszawa

Inwestor

LUX MED Onkologia Sp. z o.o.
ul. Szamocka 6; 01-748 Warszawa

Jednostka projektowa

autorskie pracownie projektowe Unimed

ul. Okrężna 33, 02-916 Warszawa
Autorskie Pracownie Projektowe
UNIMED A. Królik, L. Królik s.j.

Faza: PROJEKT WYKONAWCZY	Skala: 1:100
Branża: SANITARNA	Data: 18.02.2026
Projektant: mgr inż. Kinga Sołomko, nr upr. bud. MAZ/0068/PWBS/21	Opracował: -
Sprawdzający: mgr inż. Tomasz Dworak, nr upr. bud. St-341/84	

Tresc rysunku

RZUT PARTERU
INSTALACJA GAZÓW MEDYCZNYCH

NUMER RYSUNKU	SSE-PW-GM-01