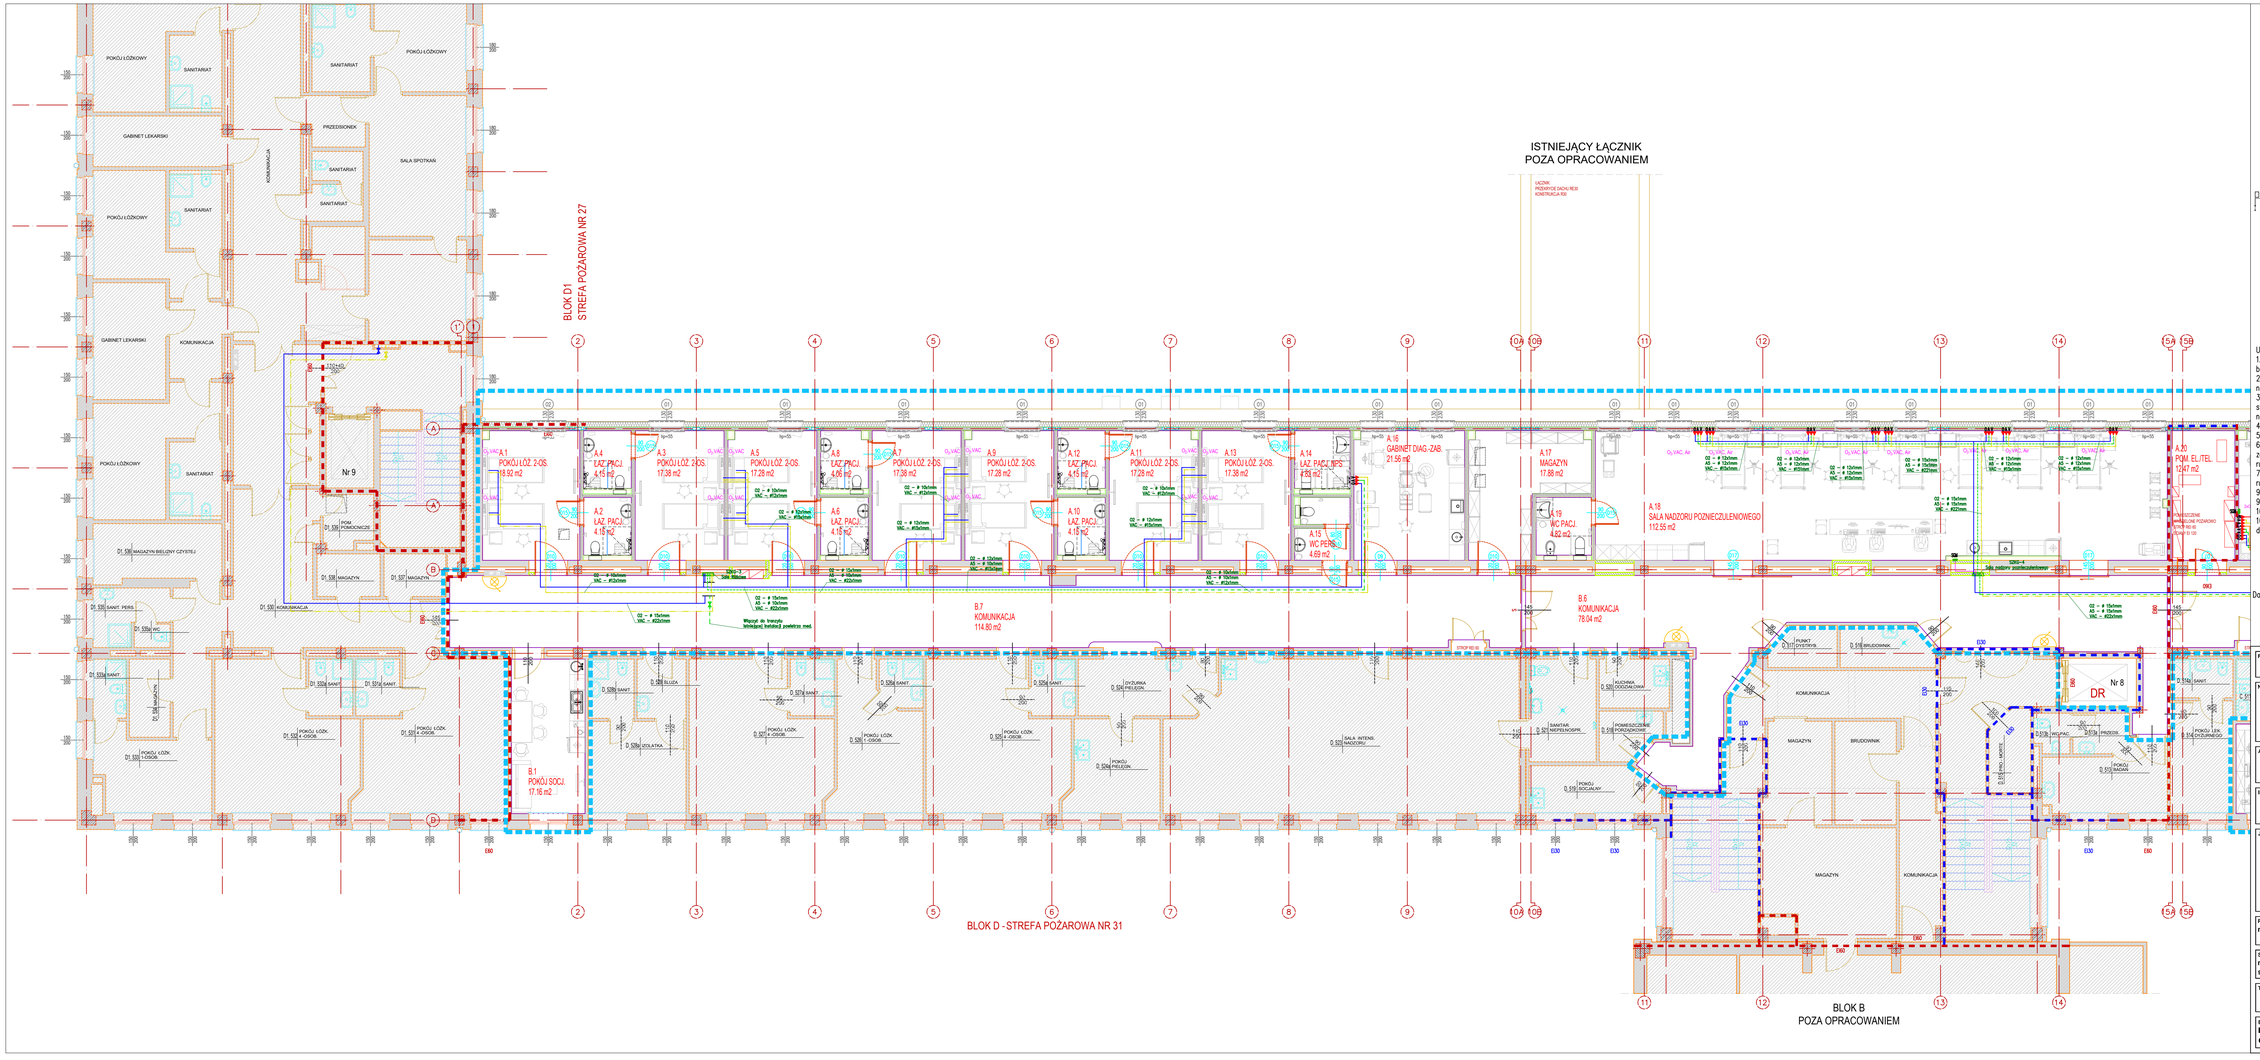

Panel medyczny poziomy nadłóżkowy

Sygnalizator Gazów Medycznych

Strefowy Zespół Kontroli Gazów Medycznych

Instalacja tlenu medycznego

Instalacja sprężonego powietrza A5

Instalacja dwutlenku węgla

Instalacja próżni

Instalacja odciągu gazów poanestetycz

O2 – ø 15x1mm — Rodzaj medium – średnica przewodu x grubość ścianki

Punkt poboru gazów medycznych

Płyta stropowa kolumny endoskopowej

Płyta stropowa kolumny anestezjologicznej

Uwagi:
1. Rysunek ten należy traktować jako integralną część dokumentacji budowlanej i należy ją czytać łącznie z opracowaniami innych branż.
2. Lokalizacja rurociągów jest przybliżona. Dokładne prowadzenie rurociągów należy określić na budowie.
3. Tam gdzie występuje sufit podwieszany należy prowadzić rurociągi pod stropem. W miejscach gdzie nie występuje sufit podwieszany rurociągi należy prowadzić w bruzdach ściennych lub w przestrzeniach ścianek lekkich.
4. Należy odtworzyć ogniodporność ścian przez które przebiegają instalacje.
5. Instalację gazów medycznych wykonać w koordynacji z innymi branżami.
6. W miejscach krzyżowania rurociągów z kablami elektrycznymi należy zachować odległość conajmniej 20 mm lub zabezpieczyć instalację rurą osłonową.
7. Miejsca przejść instalacji przez przegrody należy zabezpieczyć rurami osłonowymi.
9. Wszystkie punkty poboru gazów medycznych wykonać w standardzie AGA.
9. Wysokość montażu punktów poboru gazów wykonać na wysokości 1600 mm od posadzki.
10. Wysokość montażu SZKG wykonać na wysokości 1400 mm licząc do spodu obudowy.

Dalsza część według GM02

FAZA PROJEKTU:
PROJEKT WYROBU MEDYCZNEGO

NAZWA ZAMIERZENIA BUDOWLANEGO:
NADBUDOWA I PRZEBUDOWA CZĘŚCI BLOKU C i D
DLA POTRZEB KLINIKI GASTROENTEROLOGII
W WOJSKOWYM INSTYTUCIE MEDYCZNYM - PAŃSTWOWYM INSTYTUCIE BADAWCZYM
PRZY UL. SZASERÓW 128 W WARSZAWIE

ADRES INWESTYCJI:
ul. Szaserów 128 w Warszawie
identyfikator działki ew. 146507_8.0403.8/4

INWESTOR:
Wojskowy Instytut Medyczny - Państwowy Instytut Badawczy
ul. Szaserów 128, 04-141 Warszawa

JEDNOSTKA PROJEKTOWA:
CLIMAMEDIC
BUILD & FM
CLIMAMEDIC SPÓŁKA Z OGRANICZONĄ ODPOWIEDZIALNOŚCIĄ SP.K.
REGUŁY, UL. BODYCHA 75A 05-816 MICHAŁOWICE

PROJEKTANT:	PODPIS:
mgr inż. Jakub Kaproń	

SPRAWDZAJĄCY:	PODPIS:
mgr inż. Andrzej Michałowski 982/LB/89	

TYTUŁ RYSUNKU:
RZUT 5 PIĘTRA
INSTALACJA GAZÓW MEDYCZNYCH - WYRÓB MED.

BRANŻA:	SKALA:	DATA:	NUMER RYSUNKU:
INSTALACJE GAZÓW MED.	1:100	08.2025r.	WIM_KA_PW_MED_GM01